

2,000 A HYBRID EXAMPLE

Sizing basis

Electrical one-line


Scaled site layout

Capacity and continuity

Field verification


Electrical One-Line Diagram

2,000 A service sizing basis at 480 V, 3-phase

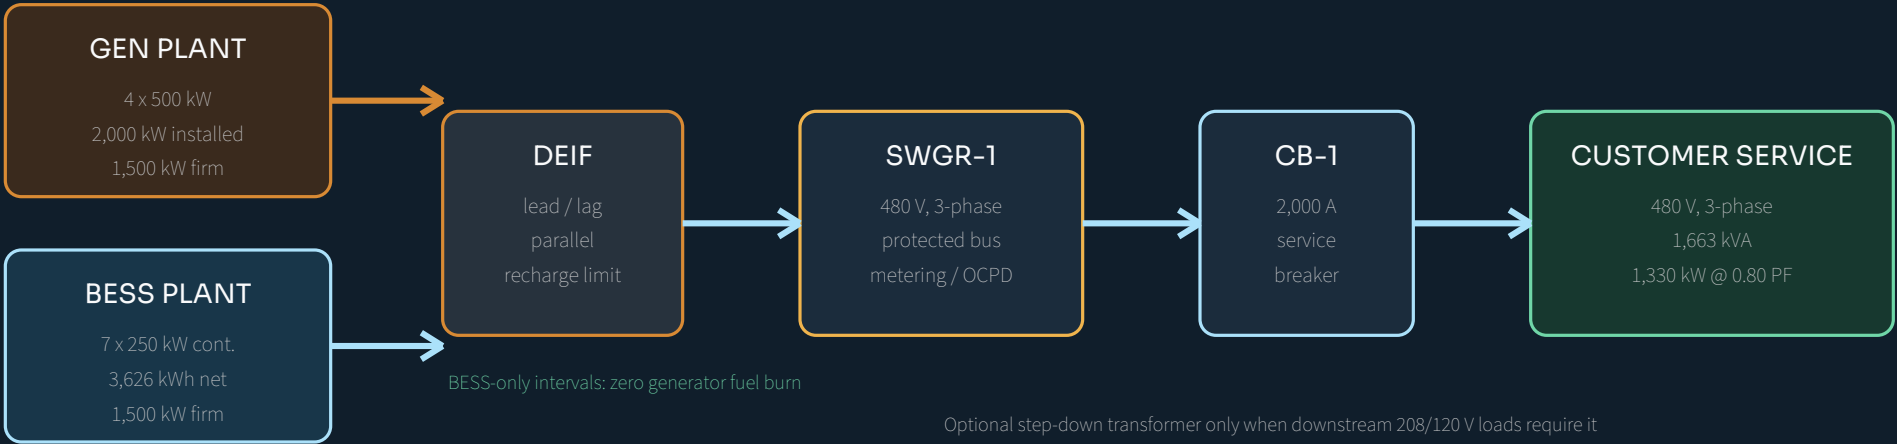

Scaled Conceptual Site Layout

Equipment bodies use current EMaaS fleet-class planning dimensions; clearances and exact delivered sizes require field verification

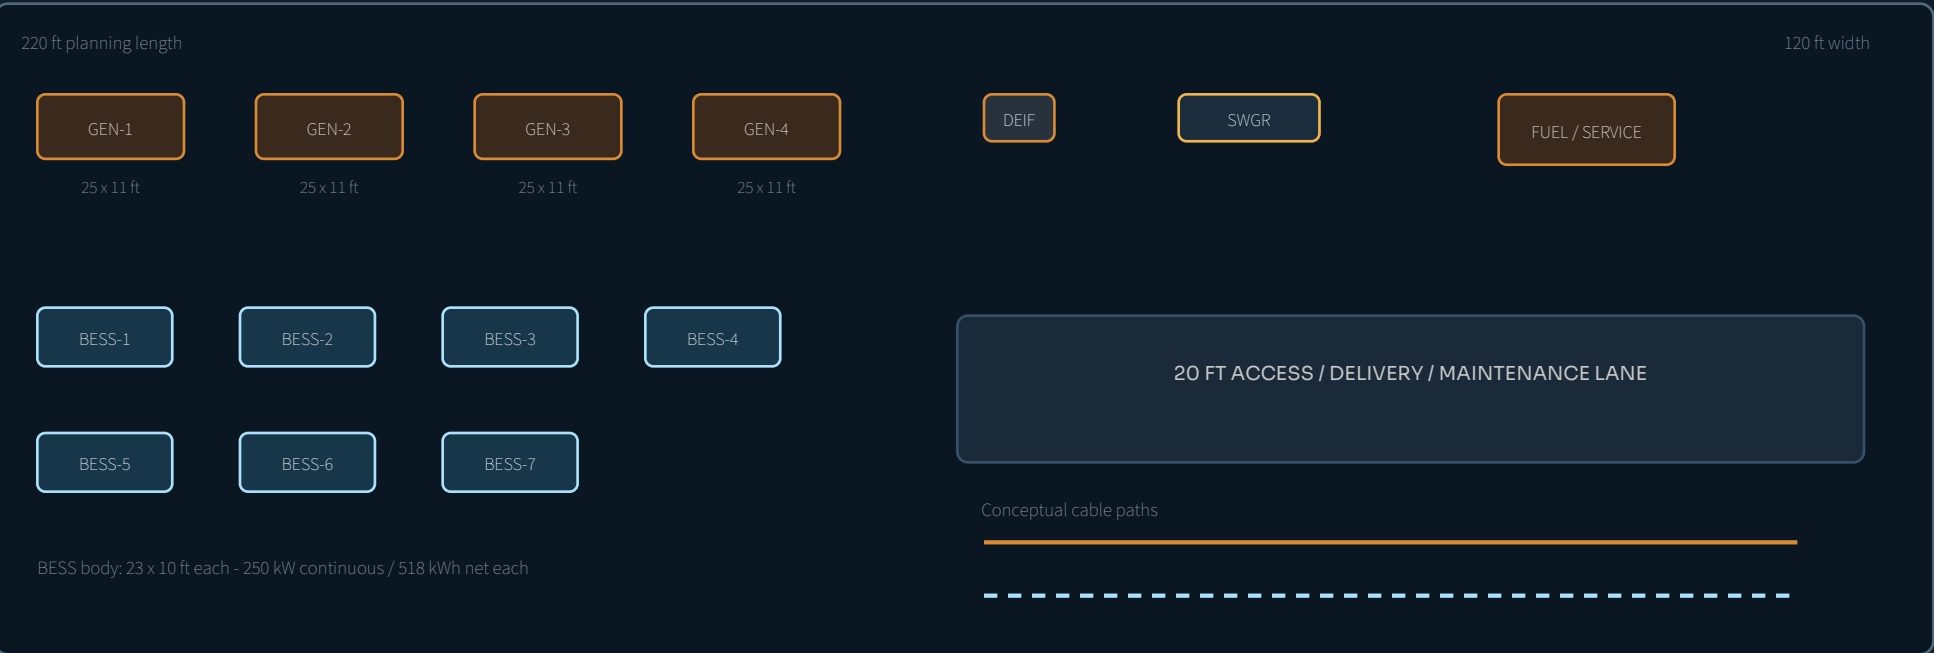

Sizing Summary

SERVICE
2,000 A

ELECTRICAL BASIS
480 V / 3-phase

PLANNING LOAD
1,330 kW

GENERATION
4 x 500 kW

2,000 kW installed
1,500 kW firm with one offline

BESS
7 x 250 kW

1,750 kW installed continuous
1,500 kW firm with one offline
3,626 kWh installed net
3,108 kWh firm net

DEIF RECHARGE LIMIT

All generators online: 670 kW
One generator offline: 170 kW

N+1 SOURCE CAPACITY

One generator or BESS unit
may be offline at 1,330 kW

Step-down: only if required

PLANNING EXAMPLE

PE and vendor verification
required before release